
COURO DE TILÁPIA E PETFISH | LOCAÇÃO DE MÁQUINAS, MOBILIÁRIO E LOUÇAS

GALPÃO PRÉ-MOLDADO | ÁREA COBERTA MODULAR: 864 m² | TERRENO HIPOTÉTICO: 3.500 m²

01 | PLANTA INTERNA - ESCALA 1:50

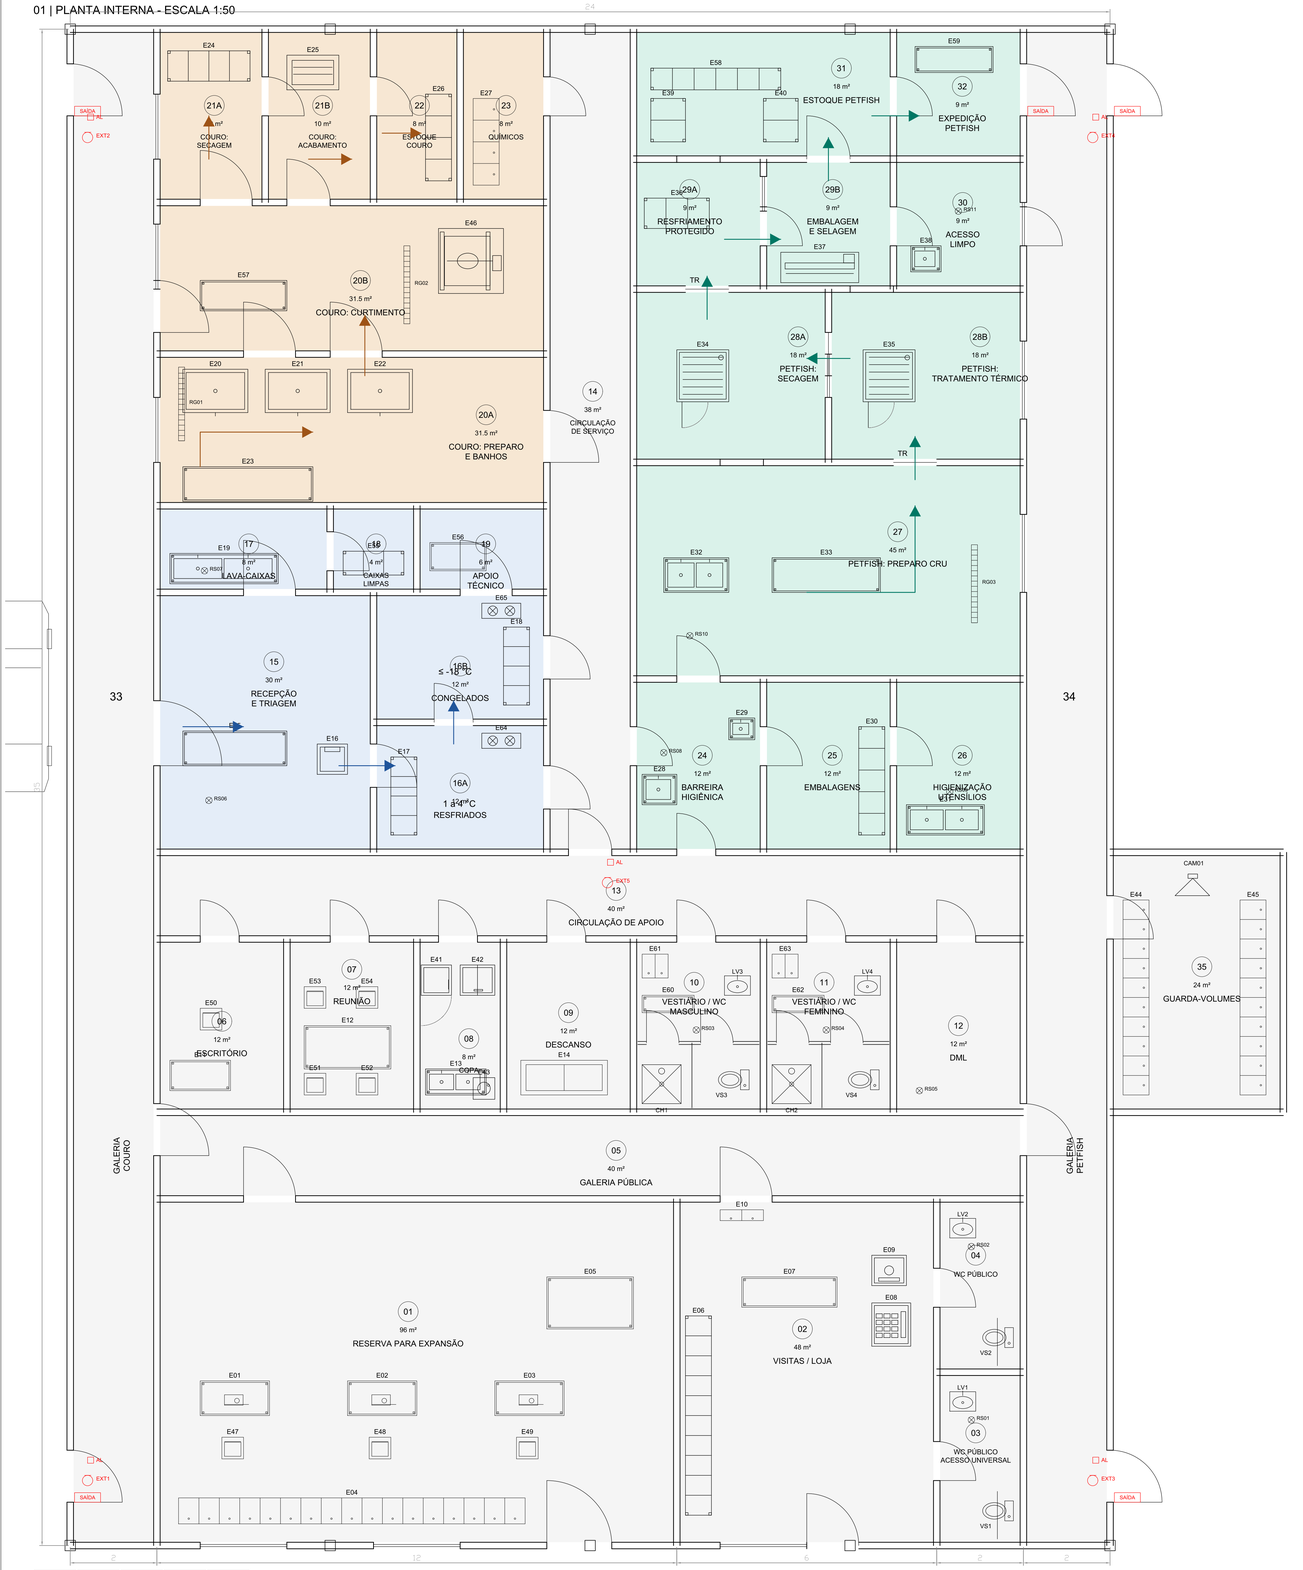

Imprimir em A0 a 100% / tamanho real. Não usar "ajustar à página".

LOCAÇÃO DOS EQUIPAMENTOS | dimensões propostas L x P, em metros

E01 Posto futuro de costura 1 | Sala 01 | 1.60 x 0.80 m
E02 Posto futuro de costura 2 | Sala 01 | 1.60 x 0.80 m
E03 Posto futuro de costura 3 | Sala 01 | 1.60 x 0.80 m
E04 Armário para peças futuras | Sala 01 | 8.00 x 0.60 m
E05 Mesa móvel de corte / eventos | Sala 01 | 2.00 x 1.20 m
E06 Expositor / loja | Sala 02 | 0.60 x 4.60 m
E07 Balcão de atendimento | Sala 02 | 2.20 x 0.70 m
E08 Máquina de bebidas e alimentos | Sala 02 | 0.90 x 1.00 m
E09 Máquina de café | Sala 02 | 0.80 x 0.70 m
E10 Unidade interna de ar-condicionado | Sala 02 | 1.00 x 0.25 m
E11 Mesa do escritório | Sala 06 | 1.40 x 0.70 m
E12 Mesa de reunião | Sala 07 | 2.00 x 1.00 m
E13 Bancada da copa com cuba | Sala 08 | 1.40 x 0.60 m
E14 Sofá de descanso | Sala 09 | 2.00 x 0.80 m
E15 Bancada de triagem | Sala 15 | 2.40 x 0.80 m
E16 Balança de recebimento | Sala 15 | 0.70 x 0.70 m
E17 Estante de caixas fechadas no frio | Sala 16A | 0.60 x 1.80 m
E18 Estante de caixas fechadas no frio | Sala 16B | 0.60 x 1.80 m
E19 Cuba de lavagem de caixas | Sala 17 | 2.50 x 0.70 m
E20 Tanque de processo 1 | Sala 20A | 1.50 x 1.00 m
E21 Tanque de processo 2 | Sala 20A | 1.50 x 1.00 m
E22 Tanque de processo 3 | Sala 20A | 1.50 x 1.00 m
E23 Bancada de descarne / preparo couro | Sala 20A | 3.00 x 0.80 m
E24 Estrutura de secagem de couro | Sala 21A | 1.90 x 0.70 m
E25 Amaciadora protegida - envelope | Sala 21B | 1.20 x 0.80 m
E26 Estante de couro acabado | Sala 22 | 0.60 x 2.00 m
E27 Armário de químicos / contenção | Sala 23 | 0.60 x 2.00 m
E28 Lavador de botas | Sala 24 | 0.80 x 0.70 m
E29 Lavatório de mãos sem acionamento manual | Sala 24 | 0.60 x 0.50 m
E30 Estante para embalagens protegidas | Sala 25 | 0.60 x 2.50 m
E31 Cuba de lavagem de utensílios | Sala 26 | 1.80 x 0.70 m
E32 Cuba de preparo PetFish | Sala 27 | 1.50 x 0.80 m
E33 Bancada de preparo PetFish | Sala 27 | 2.50 x 0.80 m
E34 Gabinete térmico / secagem - posição | Sala 28A | 1.20 x 1.20 m
E35 Gabinete térmico / secagem - posição | Sala 28B | 1.20 x 1.20 m
E36 Rack de resfriamento protegido | Sala 29A | 1.50 x 0.70 m
E37 Bancada de embalagem / seladora | Sala 29B | 1.80 x 0.70 m
E38 Lavatório de mãos sem acionamento manual | Sala 30 | 0.70 x 0.60 m
E39 Estrado de estoque PetFish | Sala 31 | 0.80 x 1.00 m
E40 Estrado de estoque PetFish | Sala 31 | 0.80 x 1.00 m
E41 Geladeira da copa | Sala 08 | 0.70 x 0.70 m
E42 Freezer da copa | Sala 08 | 0.80 x 0.70 m
E43 Bebedouro da copa | Sala 08 | 0.50 x 0.50 m
E44 Armários de guarda-volumes | Sala 35 | 0.60 x 4.50 m
E45 Armários de guarda-volumes | Sala 35 | 0.60 x 4.50 m
E46 Fulão com estrutura e motor - envelope | Sala 20B | 1.50 x 1.50 m
E47 Cadeira / posição de uso | Sala 01 | 0.50 x 0.50 m
E48 Cadeira / posição de uso | Sala 01 | 0.50 x 0.50 m
E49 Cadeira / posição de uso | Sala 01 | 0.50 x 0.50 m
E50 Cadeira / posição de uso | Sala 06 | 0.50 x 0.50 m
E51 Cadeira / posição de uso | Sala 07 | 0.50 x 0.50 m
E52 Cadeira / posição de uso | Sala 07 | 0.50 x 0.50 m
E53 Cadeira / posição de uso | Sala 07 | 0.50 x 0.50 m
E54 Cadeira / posição de uso | Sala 07 | 0.50 x 0.50 m
E55 Guarda de caixas higienizadas | Sala 18 | 1.40 x 0.55 m
E56 Bancada de controle / etiquetas | Sala 19 | 1.30 x 0.65 m
E57 Bancada de dosagem do couro | Sala 20B | 2.00 x 0.70 m
E58 Estante de produto retido / liberado | Sala 31 | 3.00 x 0.50 m
E59 Bancada de conferência da expedição | Sala 32 | 1.80 x 0.60 m
VS1 Vaso sanitário com caixa acoplada | Sala 03 | 0.74 x 0.46 m
LV1 Lavatório sanitário | Sala 03 | 0.60 x 0.45 m
VS2 Vaso sanitário com caixa acoplada | Sala 04 | 0.74 x 0.46 m
LV2 Lavatório sanitário | Sala 04 | 0.60 x 0.45 m
VS3 Vaso sanitário com caixa acoplada | Sala 10 | 0.74 x 0.46 m
LV3 Lavatório sanitário | Sala 10 | 0.60 x 0.45 m
CH1 Box de chuveiro - proposta | Sala 10 | 0.90 x 0.90 m
E60 Banco do vestiário | Sala 10 | 1.20 x 0.40 m
E61 Armário de apoio do vestiário | Sala 10 | 0.60 x 0.55 m
VS4 Vaso sanitário com caixa acoplada | Sala 11 | 0.74 x 0.46 m
LV4 Lavatório sanitário | Sala 11 | 0.60 x 0.45 m
CH2 Box de chuveiro - proposta | Sala 11 | 0.90 x 0.90 m
E62 Banco do vestiário | Sala 11 | 1.20 x 0.40 m
E63 Armário de apoio do vestiário | Sala 11 | 0.60 x 0.55 m
E64 Evaporador da câmara - posição esquemática | Sala 16A | 0.90 x 0.35 m
E65 Evaporador da câmara - posição esquemática | Sala 16B | 0.90 x 0.35 m
CAM01 Câmera do guarda-volumes (fora de sanitários) | Sala 35 | 0.30 x 0.30 m

AMBIENTES E ÁREAS MODULARES

01 Expansão reservada	96 m²	20A Couro: preparo / banhos	31.5 m²
02 Visitas / loja	48 m²	20B Couro: curtimento	31.5 m²
03 WC público / acesso universal	8 m²	21A Couro: secagem	10 m²
04 WC público complementar	8 m²	21B Couro: acabamento	10 m²
05 Galeria pública	40 m²	22 Estoque couro	8 m²
06 Escritório	12 m²	23 Químicos	8 m²
07 Reunião	12 m²	24 Barreira: área crua	12 m²
08 Copa	8 m²	25 Dep. embalagens	12 m²
09 Descanso	12 m²	26 Hig. utensílios	12 m²
10 Vest. / WC masc.	12 m²	27 PetFish: preparo cru	45 m²
11 Vest. / WC fem.	12 m²	28A Secagem com ar / saída protegida	18 m²
12 DML	12 m²	28B Tratamento térmico / entrada	18 m²
13 Circulação de apoio	40 m²	29A Resfriar protegido	9 m²
14 Circulação de serviço	38 m²	29B Embalar / selar	9 m²
15 Recepção / triagem	30 m²	30 Acesso limpo	9 m²
16A Resfriados	12 m²	31 Estoque PetFish	18 m²
16B Congelados	12 m²	32 Expedição PetFish	9 m²
17 Lava-caixas	8 m²	33 Galeria visitas: couro	70 m²
18 Caixas limpas	4 m²	34 Galeria visitas: PetFish	70 m²
19 Apoio técnico	6 m²	35 Guarda-volumes / acesso monitorado	24 m²

SÍMBOLOS E LEITURA

VS = vaso sanitário | LV = lavatório | CH = chuveiro.

RS = ralo sifonado com tampa fechável | RG = ralo-grelha.

E01... = equipamentos e mobiliário: conferir legenda acima.

EXT = extintor proposto | AL = alarme manual | SAÍDA = sinalização.

Círculo de ambiente identifica a sala no quadro.

Representação em planta; dimensões são propostas, sem marca/modelo.

Cotas em metros, por eixos; paredes de 0,15 m propostas.

Não inferir capacidade de produção, carga elétrica ou aprovação sanitária.

HIGIENE E FLUXO

Couro e PetFish permanecem separados. Peles tratadas quimicamente não retornam ao alimento.
Frio em dois regimes, lotes identificados, entrada do cru e acesso limpo distintos.
O setor seco requer limpeza controlada: os ralos não são pontos de descarte de sólidos ou de químicos.
Funcionários: vestiários e sanitários M/F com banho. CFTV apenas no guarda-volumes/acessos.

COURO: preparo / banhos > curtimento > secagem > acabamento > estoque.

PETFISH: preparo cru > térmico > secagem > resfriar > embalar > estoque > expedir.

COURO | PETFISH | RECEPÇÃO / FRIO

Setas: sentido das etapas. Transferências sujeitas às barreiras e aos acessos indicados.

EUCLIDES JR | UFS 202200026614 | Tecnologia do Pescado 2

Professor José Milton Barbosa | São Cristóvão - SE | Próximo à FedEx

Coordenadas informadas: -10.9210893676, -37.0913511411

A0 | R15 | FOLHA 1/03 | 25/10/2026 | ESCALAS INDICADAS

ESTUDO ACADÊMICO | RT / ART-RRT: A DEFINIR | NÃO LIBERADO PARA OBRA

COURO DE TILÁPIA E PETFISH | ÁREA EXTERNA, COBERTURA E FACHADA


GALPÃO PRÉ-MOLDADO | ÁREA COBERTA MODULAR: 864 m² | TERRENO HIPOTÉTICO: 3.500 m²

02 | IMPLANTAÇÃO INTEGRADA - ESCALA 1:100


Terreno 50 x 70 m. Limites e orientação não foram levantados em campo.



03 | COBERTURA PROPOSTA - 1:150

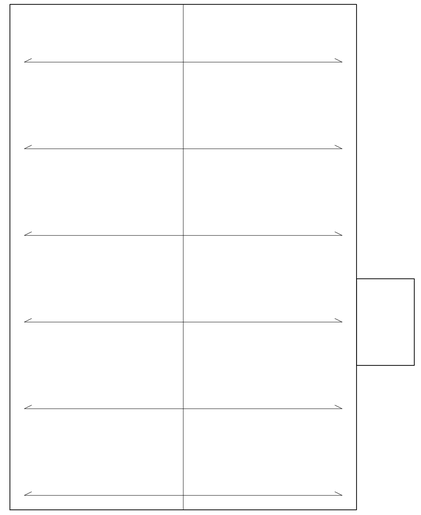

04 | FACHADA FRONTAL - 1:100

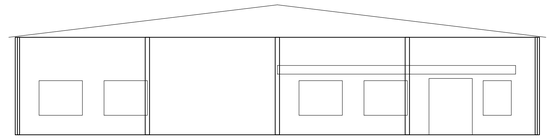

ÁREAS DO CONJUNTO

Terreno hipotético: 3.500 m²

Coberto nominal: 864 m²

Descoberto: 2.636 m²

Núcleo e galerias: 840 m²

Guarda-volumes: 24 m²

5 vagas de carros + faixa lateral

Fiorino no recebimento

Caminhão referência: 9,00 x 2,60 m

ITENS EXTERNOS E INTERFACES

Acesso público separado da entrada de serviço.

Passeio de visitantes protegido junto ao bloco frontal.

Recebimento junto à triagem; expedição no lado PetFish.

Pátio traseiro e via lateral reservados à circulação de serviço.

Reserva técnica: água, efluentes e resíduos com acessos próprios.

Trajetória de giro/manobra e veículo de projeto: verificar em projeto viário.

Pilares e cobertura são posições gráficas; fundações e estrutura a calcular.

As coordenadas informadas localizam um ponto, não os limites da propriedade.

PREMISSAS DA IMPLANTAÇÃO

O projeto preserva expansão para três postos futuros de costura e armários, loja e espera com climatização, copa com geladeira/freezer/bebedouro, descanso e apoio de gestão.
A área de expansão pode receber eventos após reorganização das máquinas e avaliação da lotação.
Levantamento topográfico, norte geográfico, drenagem do lote, acessibilidade e aprovação municipal permanecem necessários.

COURO | PETFISH | RECEPÇÃO / FRIO

Setas: sentido das etapas. Transferências sujeitas às barreiras e aos acessos indicados.

EUCLIDES JR | UFS 202200026614 | Tecnologia do Pescado 2

Professor José Milton Barbosa | São Cristóvão - SE | Próximo à FedEx

Coordenadas informadas: -10.9210893676, -37.0913511411


A0 | R15 | FOLHA 2/03 | 25/10/2026 | ESCALAS INDICADAS

ESTUDO ACADÊMICO | RT / ART-RRT: A DEFINIR | NÃO LIBERADO PARA OBRA


COURO DE TILÁPIA E PETFISH | PONTOS DE INFRAESTRUTURA E SANITÁRIOS

GALPÃO PRÉ-MOLDADO | ÁREA COBERTA MODULAR: 864 m² | TERRENO HIPOTÉTICO: 3.500 m²


05 | PONTOS E TRAÇADOS PRELIMINARES - 1:50

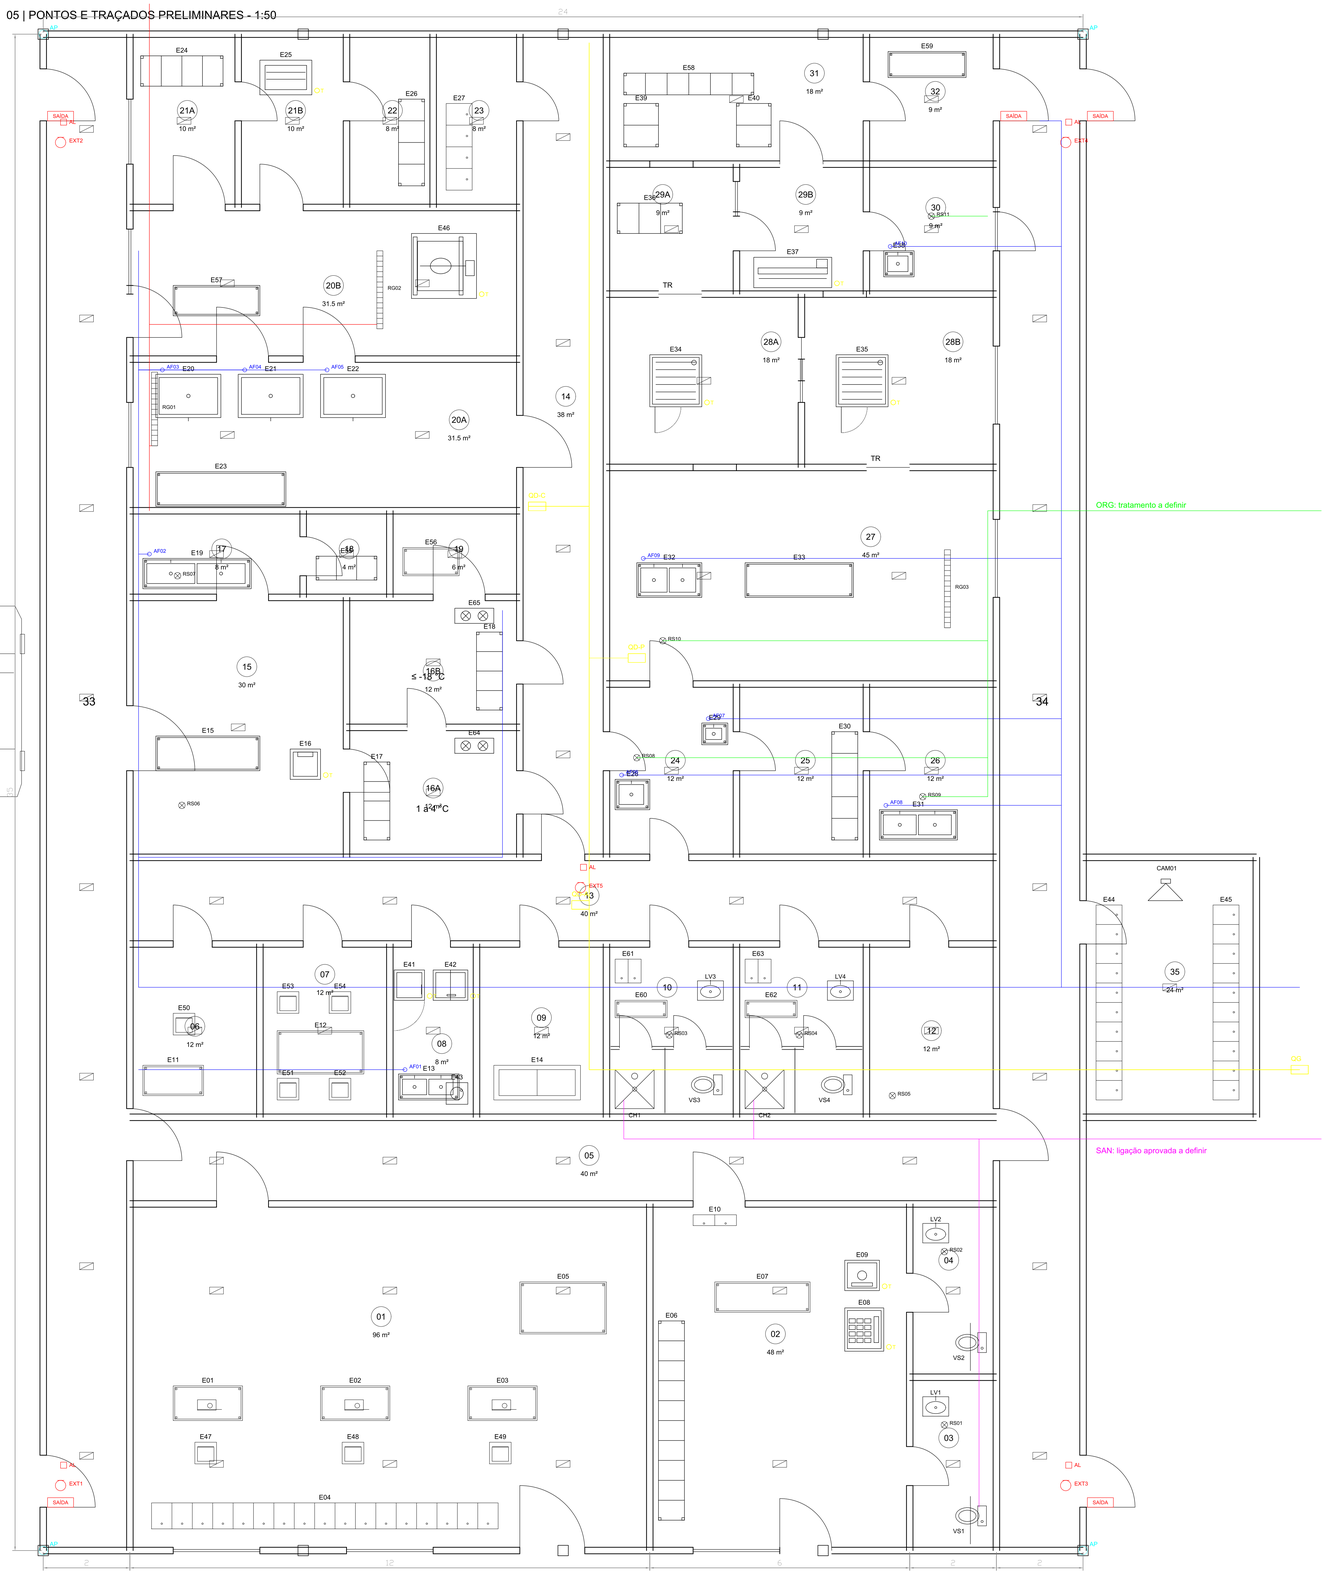

06 | VESTIÁRIOS / SANITÁRIOS M/F - 1:20

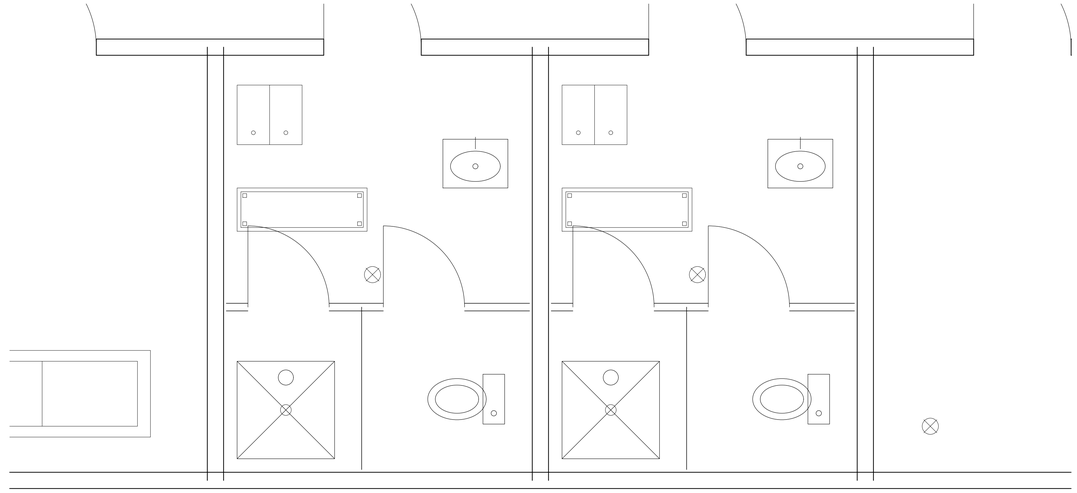

07 | SANITÁRIOS PÚBLICOS - 1:20

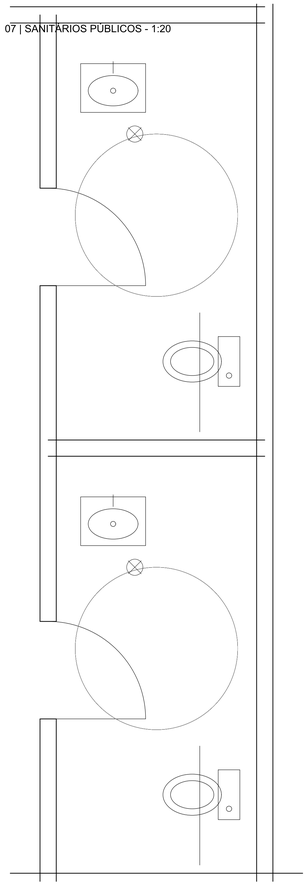

LEGENDA DE INFRAESTRUTURA

- AF: água potável e pontos de consumo
- IND: efluente do curtume, segregado
- ORG: efluente orgânico da linha PetFish
- SAN: esgoto sanitário
- AP: águas pluviais / condutores
- QG / QD: quadros e alimentação proposta
- Símbolo retangular com diagonal: luminária
- EXT / AL / SAÍDA: pontos candidatos

LIMITES DESTA PRANCHA

Traçados servem à compatibilização espacial. Não definem diâmetros, cargas, proteções, declividades ou tratamento de efluentes.
Banhos incompatíveis exigem segregação por POP e projeto específico. Não há autorização de lançamento no ambiente.
As folgas de uso e manutenção são distintas da área da máquina. Confirmar no manual selecionado.
Verificar acessibilidade integral, áreas de transferência, portas e barras com responsável habilitado.
Incêndio, estrutura, elétrica e hidráulica precisam de projetos executivos e aprovações próprios.

EUCLIDES JR | UFS 202200026614 | Tecnologia do Pescado 2

Professor José Milton Barbosa | São Cristóvão - SE | Próximo à FedEx

Coordenadas informadas: -10.9210893676, -37.0913511411

A0 | R15 | FOLHA 3/03 | 25/10/2026 | ESCALAS INDICADAS

ESTUDO ACADÊMICO | RT / ART-RRT: A DEFINIR | NÃO LIBERADO PARA OBRA